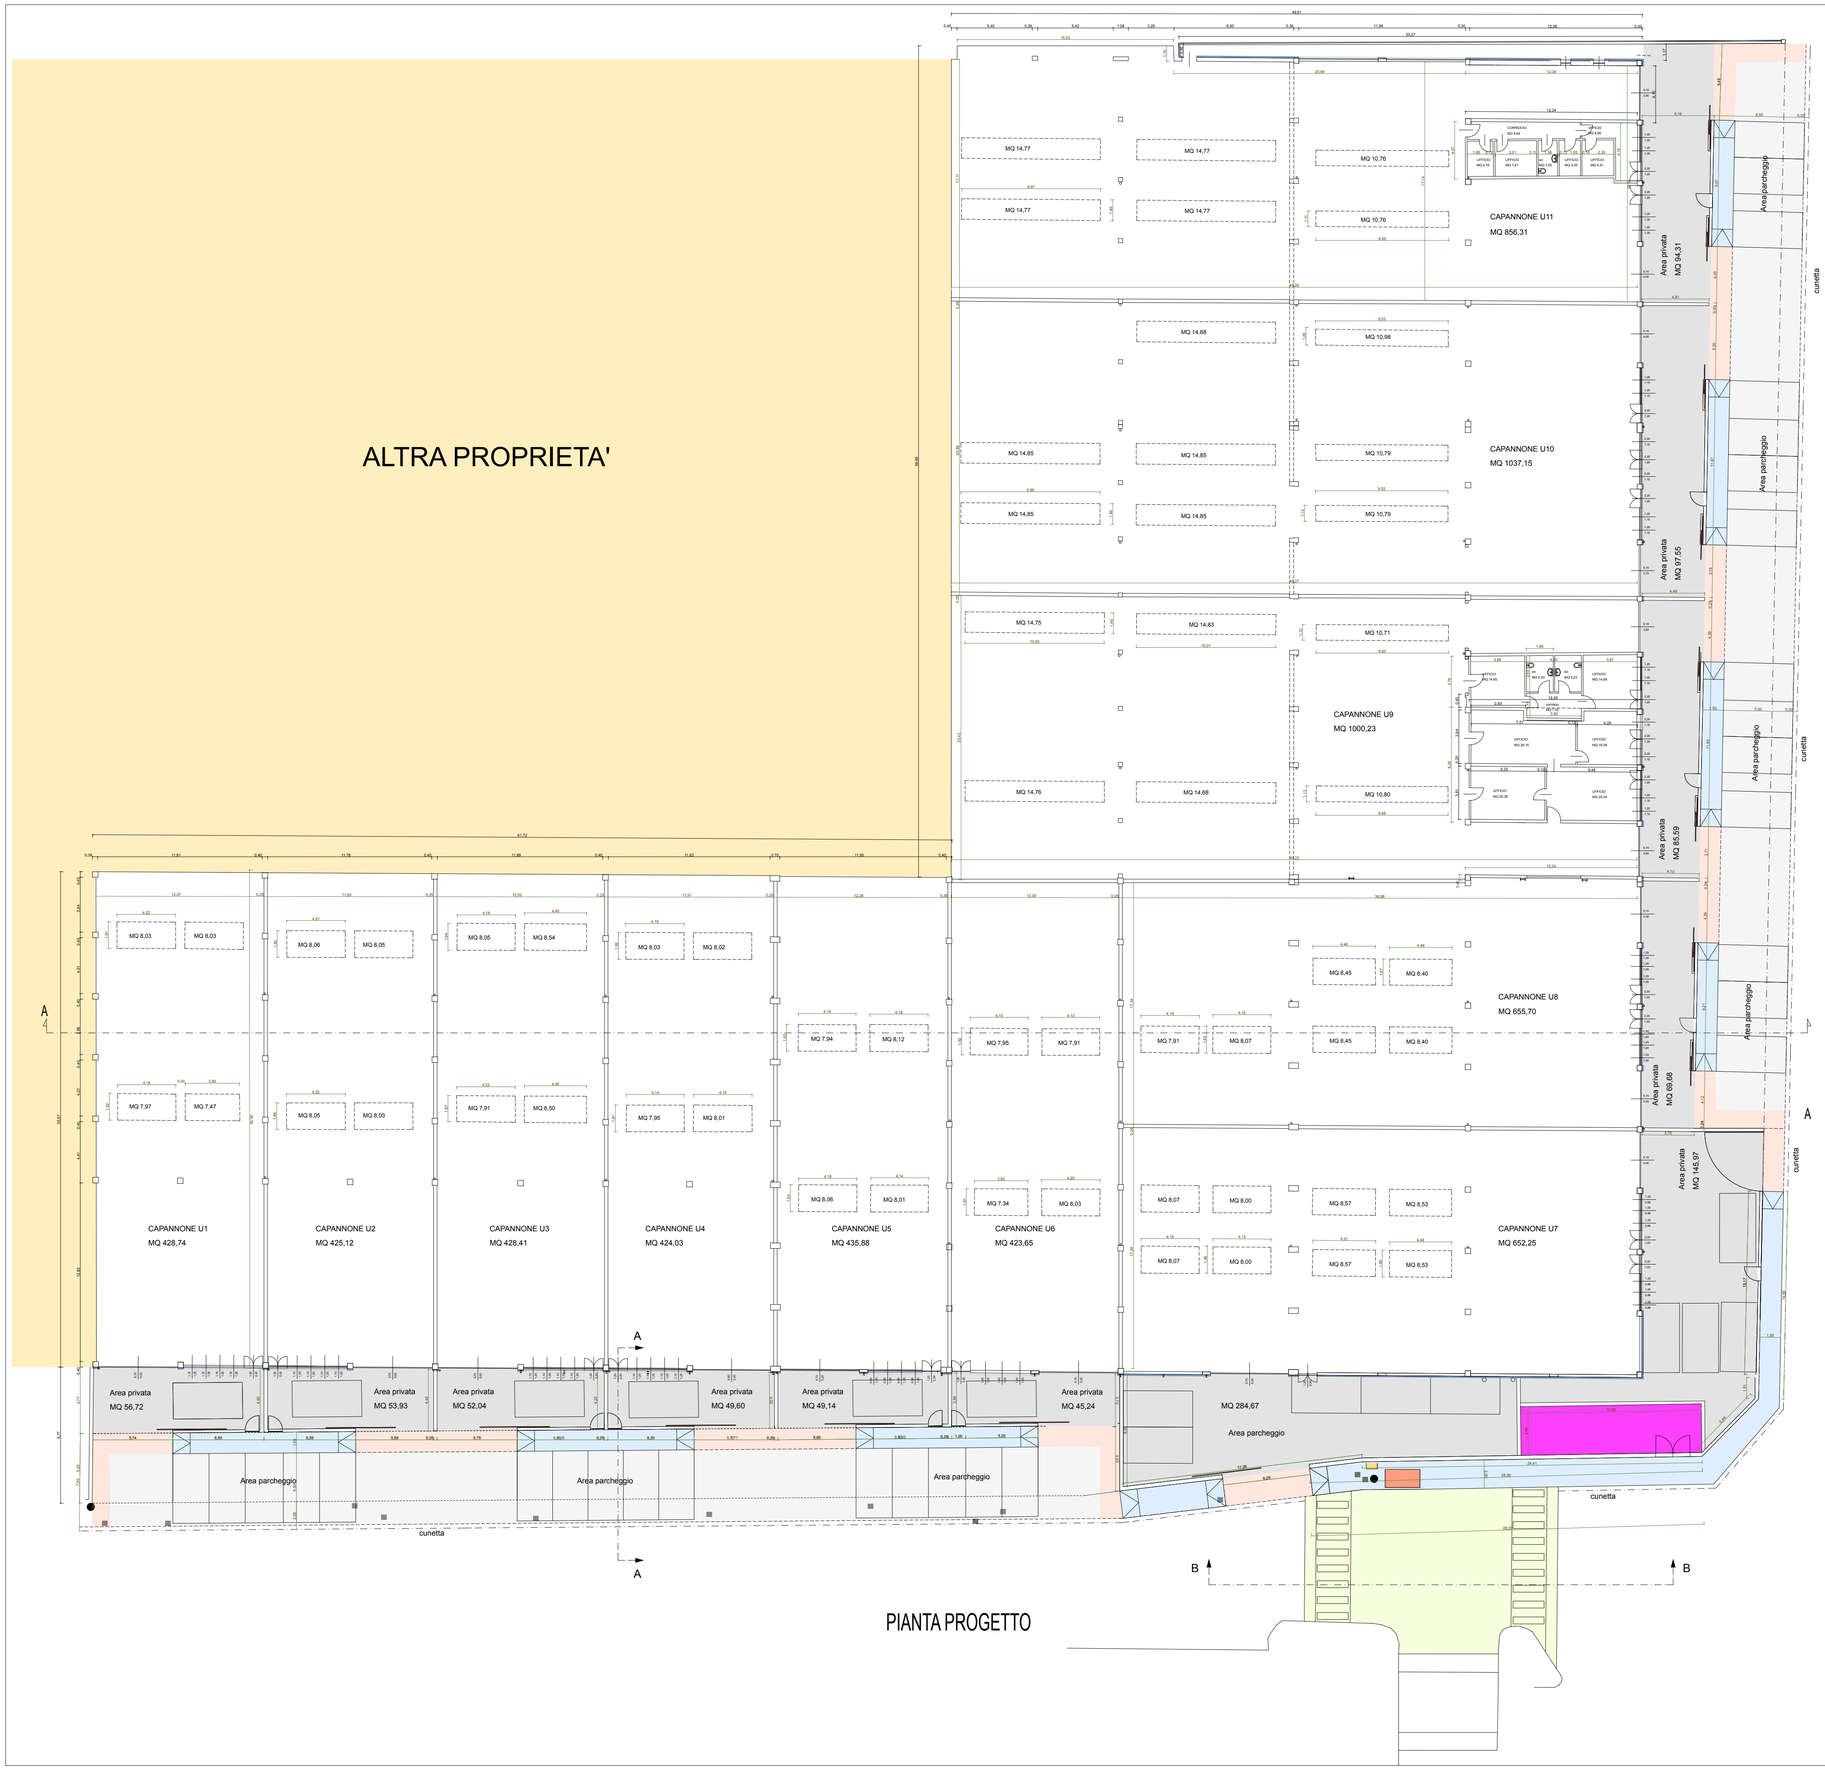

PIANTA PROGETTO

Area privata
in cemento

Area parcheggio

attraversamento pedonale
a raso, con segnaletica

marciapiede rialzato

doppio attraversamento
pedonale rialzato

nuova cabina elettrica
10,50x3,50
locale contattori
2,5x3,50

S & G
architettura
Arch. Massimo Guerrato

25124 Brescia piazza almici 15
tel. 030 5030315
www.studiumguerrato.com
massimoguerrato70@gmail.com

comune di Paderno Dugnano

Segnalazione Certificata Inizio Attività
Alternativa al Permesso di Costruire
D.P.R. 380/2001

Via Como angolo via Serrati

PERMESSO DI COSTRUIRE
CONVENZIONATO

committente
Immobiliare Biancospini S.r.l.
Piazza Duca D'Aosta n 10 20124

titolo
PLANIMETRIA PROGETTO

tavola n.
5a

scala
1:100

data
20 - 04 - 2024

aggiornamenti
01 - 07 - 2024
10 - 10 - 2025

protocollo-numero progetto
C.E. N.V 001